


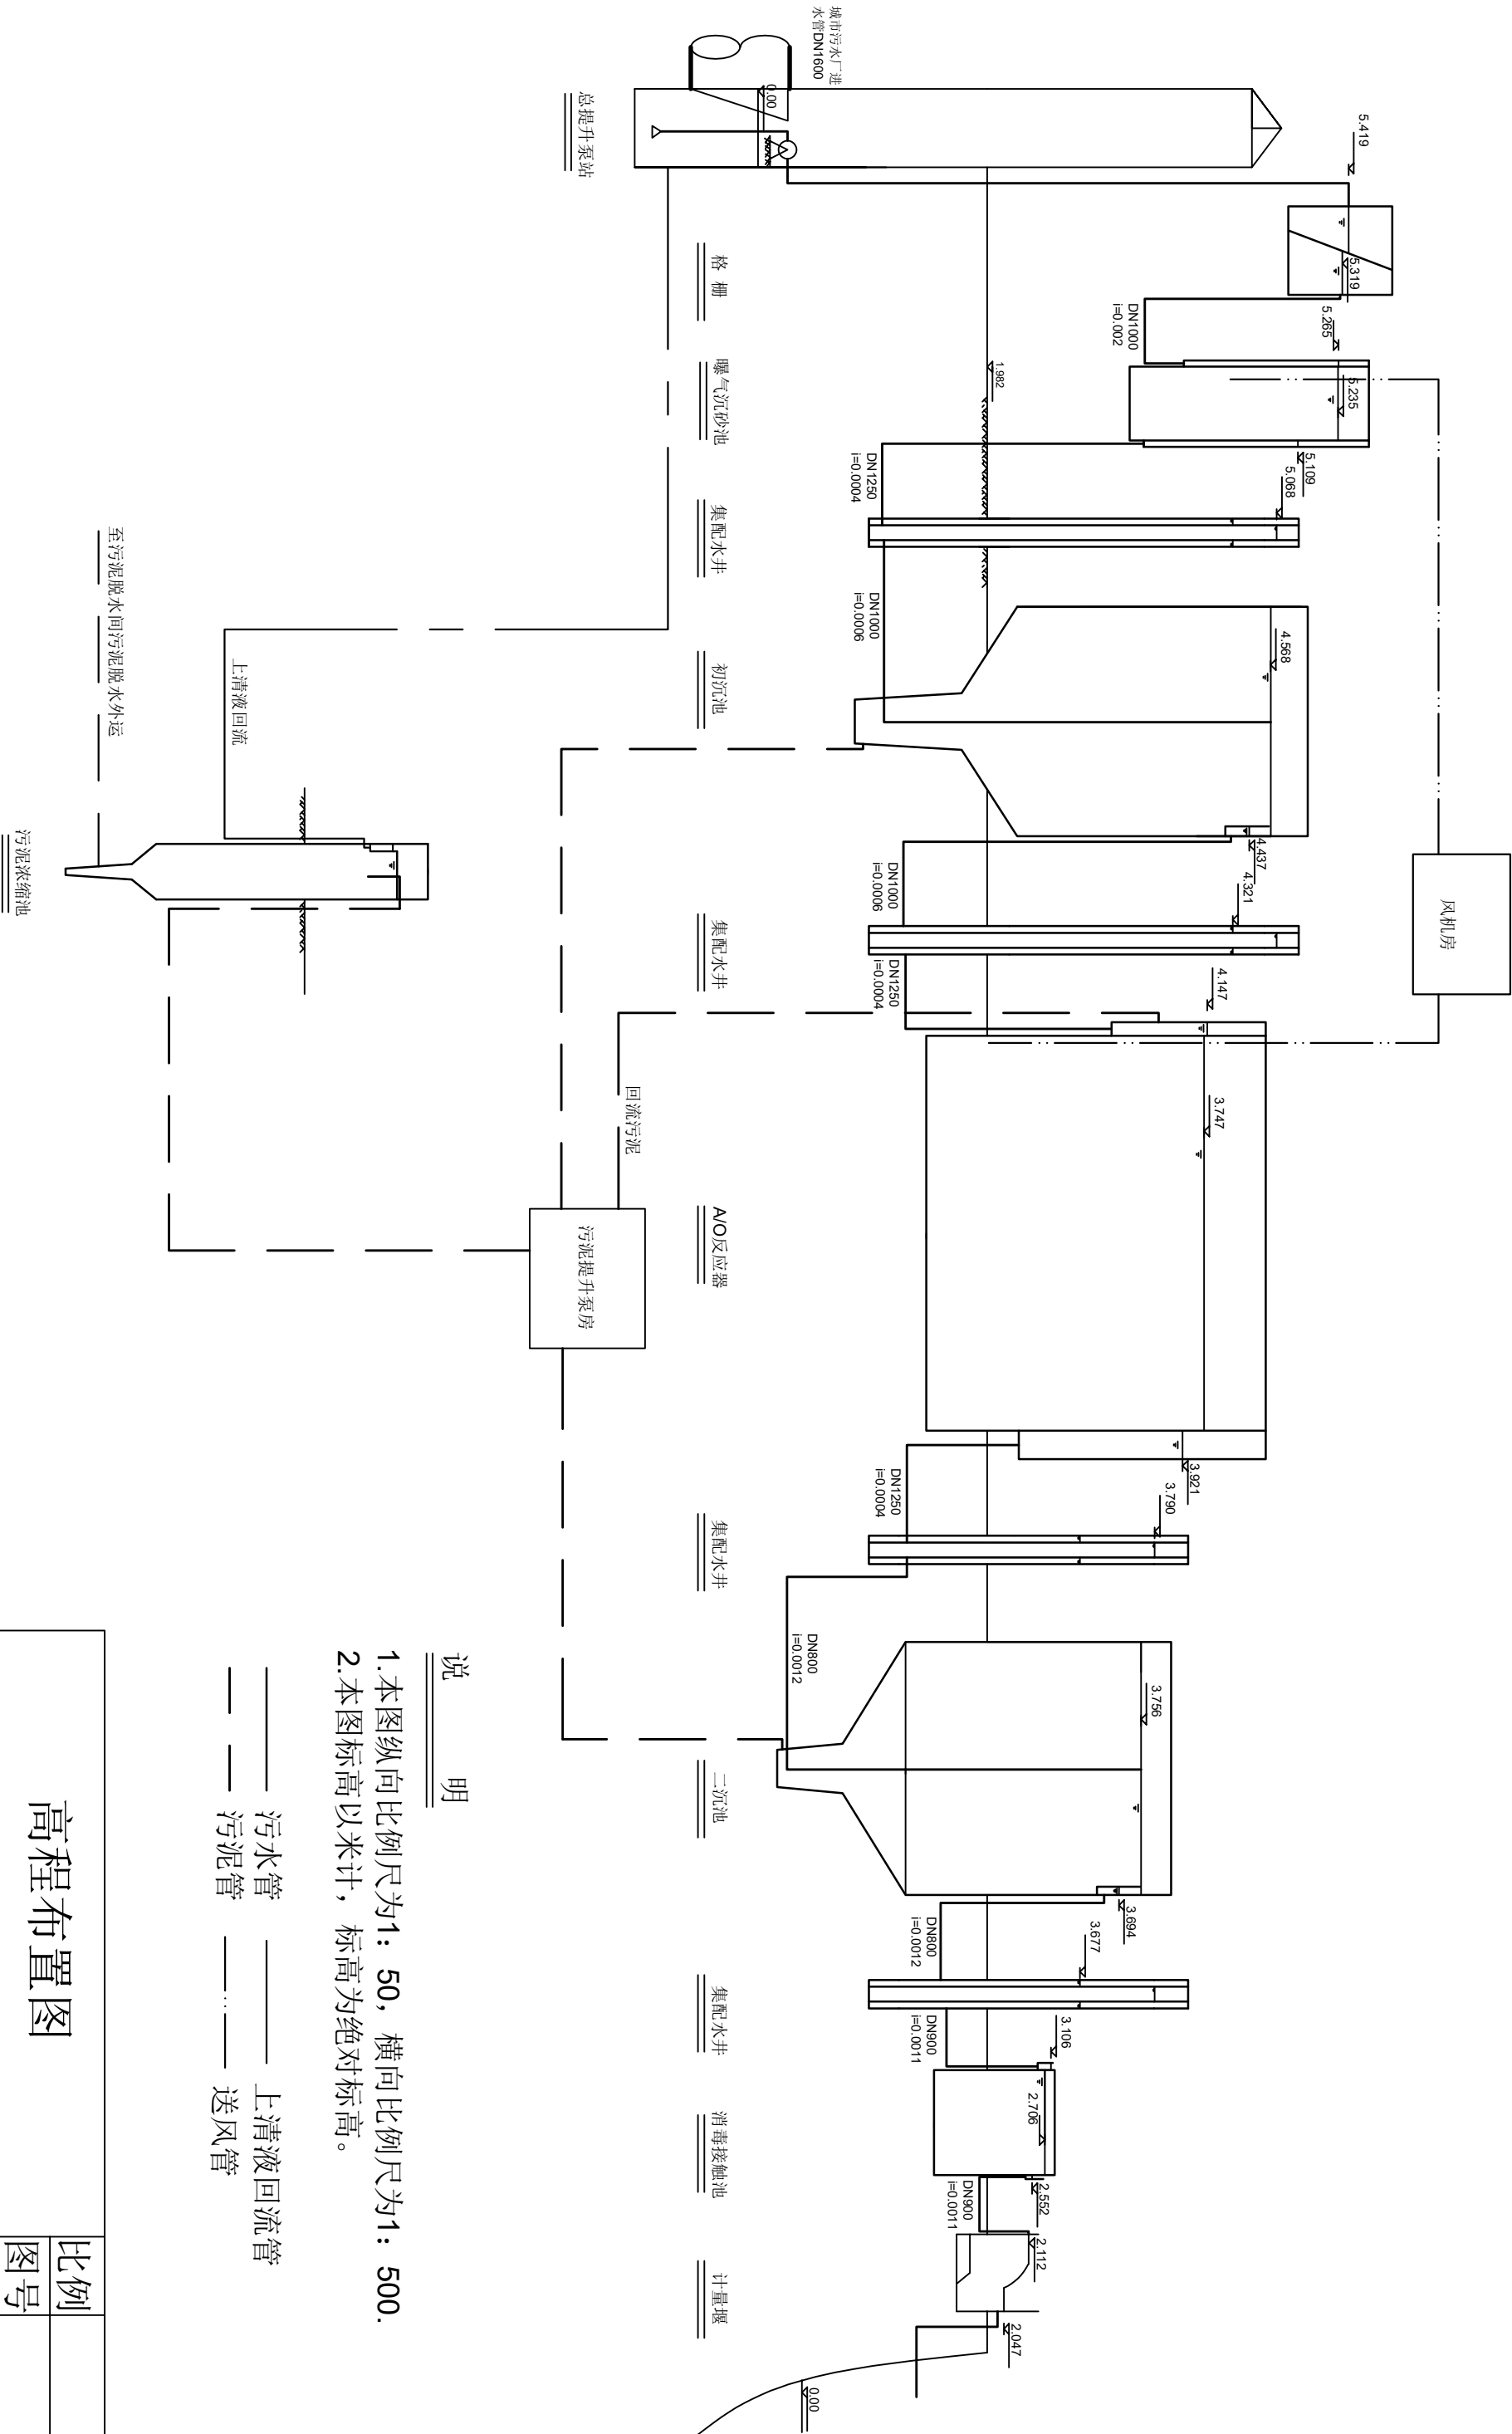

说明

1. 本图纵向比例尺为1: 50，横向比例尺为1: 500.
2. 本图标高以米计，标高为绝对标高。

—— 污水管
—— 污泥管
—— 上清液回流管
—— 送风管

高程布置图			比例	图号
制图	孙紫薇	2201060201		
指导老师	暴瑞玲			
河海大学				